PLANTA GENERAL - BASES AISLADAS

Escala 1:100

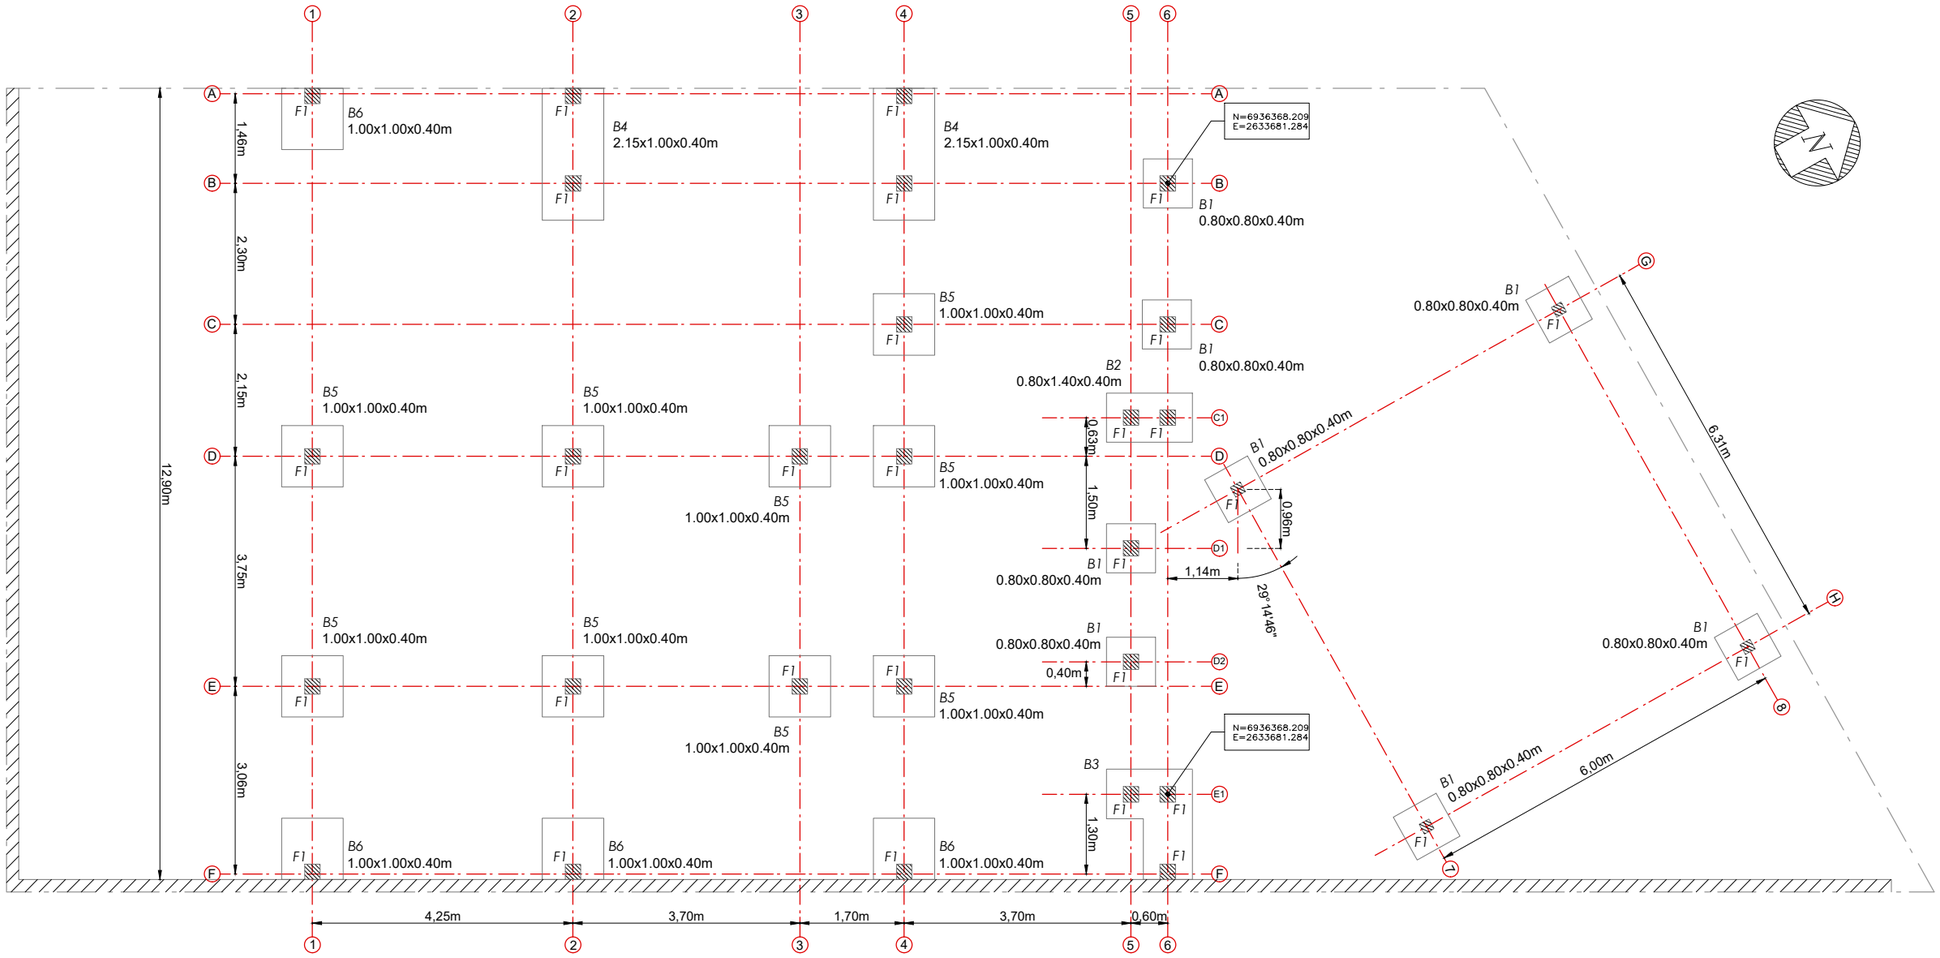

MATERIALES:

a.- HORMIGON ARMADO, f`c = 15 MPA
b.- HORMIGON DE LIMPIEZA, f`c = 8 MPA
c.- HORMIGON VEREDA, f`c = 15 MPA
d.- ACERO DE REFUERZO:
MALLA SIMA ELECTROSOLDADA.
T-500 - fy = 500MPa
ADN420: 420 Mpa.

RECUBRIMIENTO DE HORMIGON:

FUNDACIONES: 50mm.
FUSTES: 35mm
COLUMNAS: 15mm
VIGAS: 25mm

NOTAS GENERALES:

1_DIMENSIONES EN m., NIVELES EN m.
2_ABREVIATURAS:
N.T.N. = NIVEL TERRENO NIVELADO
N.S.H. = NIVEL SOBRE HORMIGÓN
N.I.H. = NIVEL INFERIOR HORMIGÓN
N.S.P. = NIVEL SOBRE PERFIL
N.P.T. = NIVEL PISO TERMINADO
B. = BASE
V.F. = VIGA DE FUNDACIÓN
F. = FUSTE
C.= COLUMNA
SUP. = SUPERIOR
INF. = INFERIOR

TRABAJAR CON PLANOS:

AR-010100-0216-CI-DAL-0100-001_0
AR-010100-0216-CI-DAL-0100-002_0
AR-010100-0216-CI-DAL-0100-003_0
AR-010100-0216-CI-DAL-0100-004_0
AR-010100-0216-CI-DAL-0100-005_0

MATERIAL DE RELLENO:

ESTARÁ CONSTITUIDOS POR MATERIAL INERTE PERTENECIENTES A MATERIAL APTO EXCAVADO EN ZONA DE OBRA, DEBIDAMENTE COMPACTADO.

EL MATERIAL DEBE SER REDUCIDO EN SALES SOLUBLES, PARA CONSTITUIRSE EN UN PRIMER RECEPTOR ESTABLE ANTE LA EVENTUAL CAÍDA DE AGUA DE LLUVIA O CUALQUIER OTRA FUENTE.

DEBE CUMPLIR ADICIONALMENTE CON LOS SIGUIENTES PUNTOS:

- TAMAÑO MÁXIMO 2".
- EL MATERIAL SE COLOCARÁ EN CAPAS DE 0,20m DE ESPESOR COMO MÁXIMO.
- DENSIDAD >90% PROCTOR MODIFICADO.
- LA COMPACTACIÓN SERÁ EJECUTADA CON EQUIPOS MANUALES, TALES COMO UNA PLACA O PISÓN.

EN EL CASO DE RELLENOS ESTRUCTURALES LOCALIZADOS ADYACENTES A ESTRUCTURAS DE HORMIGÓN, EL RELLENO DEBERÁ INICIARSE UNA VEZ QUE EL HORMIGÓN HAYA DESARROLLADO EL 75% DE SU RESISTENCIA A 28 DÍAS, O DESPUÉS DE 14 DÍAS DE HORMIGONADO Y UNA VEZ RETIRADOS LOS MOLDAJES, RETAPADOS LOS TENSORES, COLOCADA LA IMPERMEABILIZACIÓN DE FUNDACIONES (SUJETO A CONFIRMACIÓN EN PLANOS DE DISEÑO) Y RECIBIDA LA LIMPIEZA DE LAS SUPERFICIES

LO INDICADO ANTERIORMENTE ES INDICATIVO SIENDO EL CONSTRUCTOR EL RESPOSABLE FINAL DE LOS TRABAJOS BASADO EN SUS ESTUDIOS DE LABORATORIO EN SITIO Y EL REPORTE DE CLASIFICACION DE SUELOS.

NOTA - MOVIMIENTO DE SUELOS

SE ADOPTÓ FUNDACIONES CON ZAPATAS AISLADAS ARRIOSTRADAS CON VIGAS, CUYO PLANO DE ASIENTO ESTA UBICADA EN LA COTA (-1,20 m) REFERIDO AL NIVEL DE TERRENO NATURAL.

SE COLOCARA VEREDA PERIMETRAL POR EVENTUALES INGRESO DE AGUA SUPERFICIAL POR LLUVIA.

EMITIDO PARA
CONSTRUCCION
FECHA:_____ APROB. POR:_____

CUADRO DE REVISIONES

REVISION	ELAB.	REV.	APR.	FECHA
0	M.S.	A.L.	M.S.	21/09/25
1	M.S.	A.L.	M.S.	23/03/26

AURO S.R.L.

"Este documento y la informacion contenida en el, es confidencial y propiedad de AURO SRL. No puede ser copiada, divulgada o utilizada sin el consentimiento por escrito de AURO S.R.L."

PROYECTO INTI ANAHI ZARATE

Plano Estructural de Fundaciones

Bases Aisladas - Geometria

CODIGO: AR - 010100 - 0216 - CI - DGA - 0100 - 001

ELABORO	REVISO	APROBO	REVISION	ESCALA	HOJA Nº
M.S. 23/03/26	A.L. 23/03/26	M.S. 23/03/26	1	S/E	1 / 1